


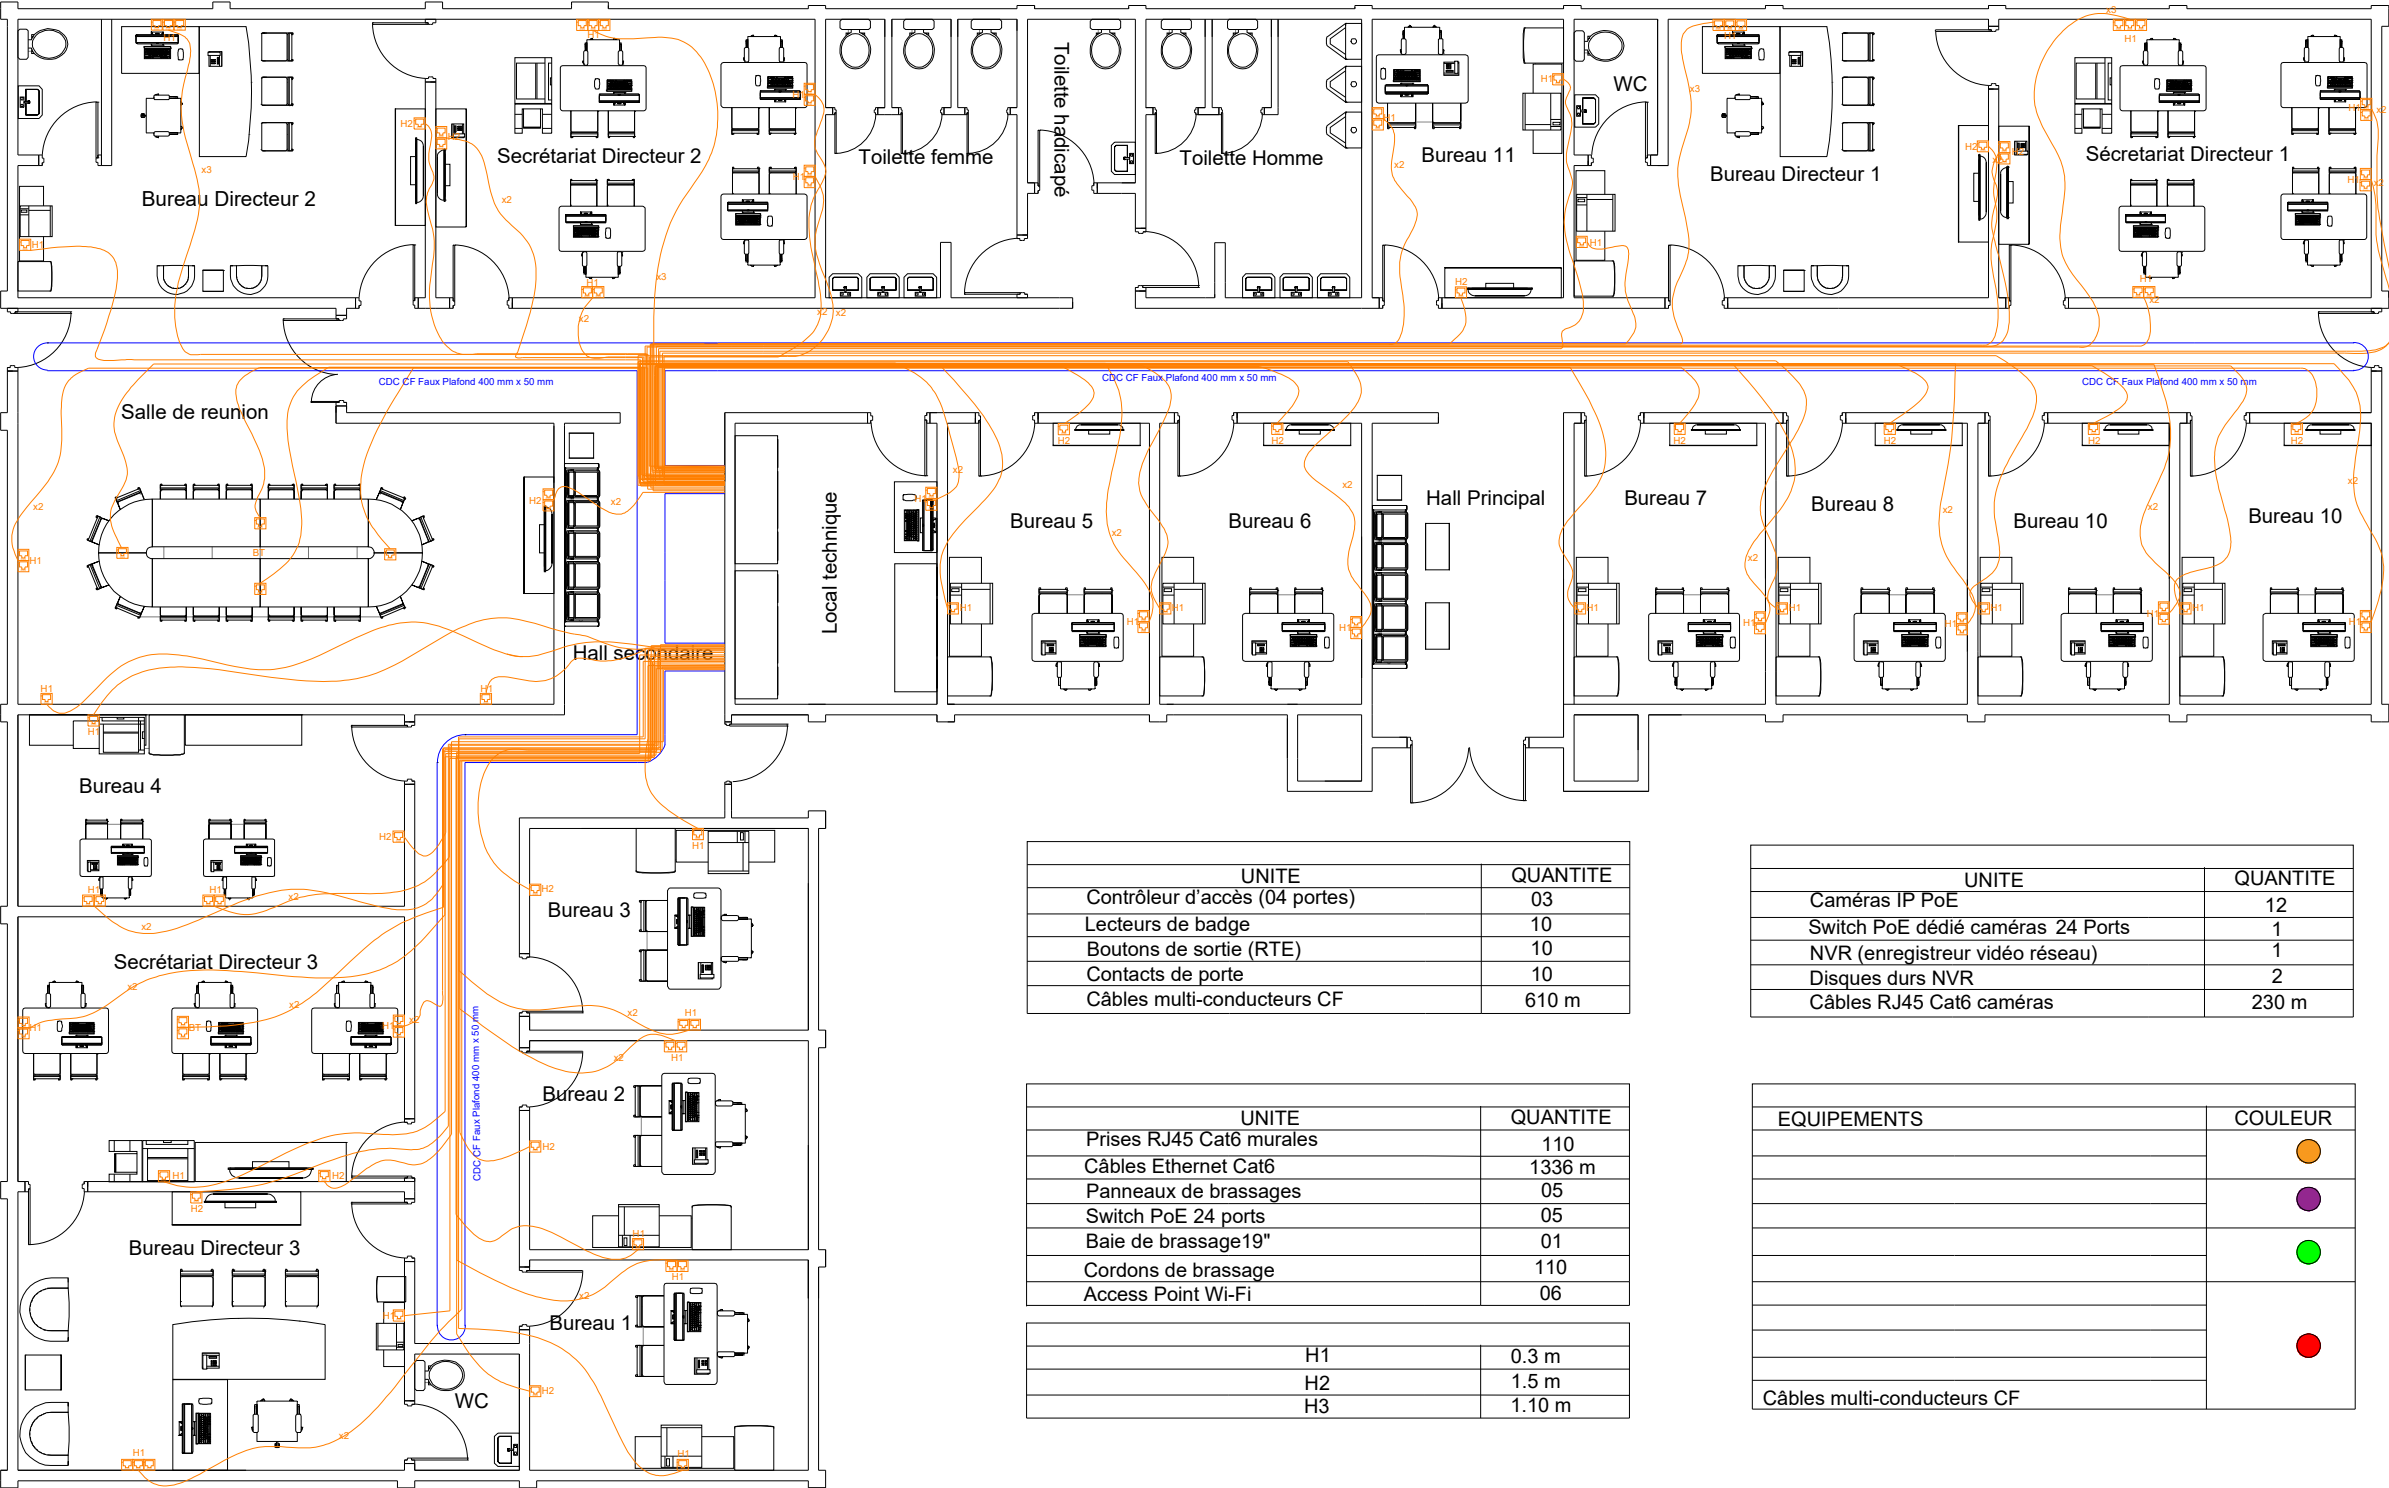

UNITE	QUANTITE
Contrôleur d'accès (04 portes)	03
Lecteurs de badge	10
Boutons de sortie (RTE)	10
Contacts de porte	10
Câbles multi-conducteurs CF	610 m

UNITE	QUANTITE
Caméras IP PoE	12
Switch PoE dédié caméras 24 Ports	1
NVR (enregistreur vidéo réseau)	1
Disques durs NVR	2
Câbles RJ45 Cat6 caméras	230 m

UNITE	QUANTITE
Prises RJ45 Cat6 murales	110
Câbles Ethernet Cat6	1336 m
Panneaux de brassages	05
Switch PoE 24 ports	05
Baie de brassage 19"	01
Cordons de brassage	110
Access Point Wi-Fi	06

H1	0.3 m
H2	1.5 m
H3	1.10 m

EQUIPEMENTS	COULEUR
	Orange
	Pourpre
	Vert
	Rouge
Câbles multi-conducteurs CF	