


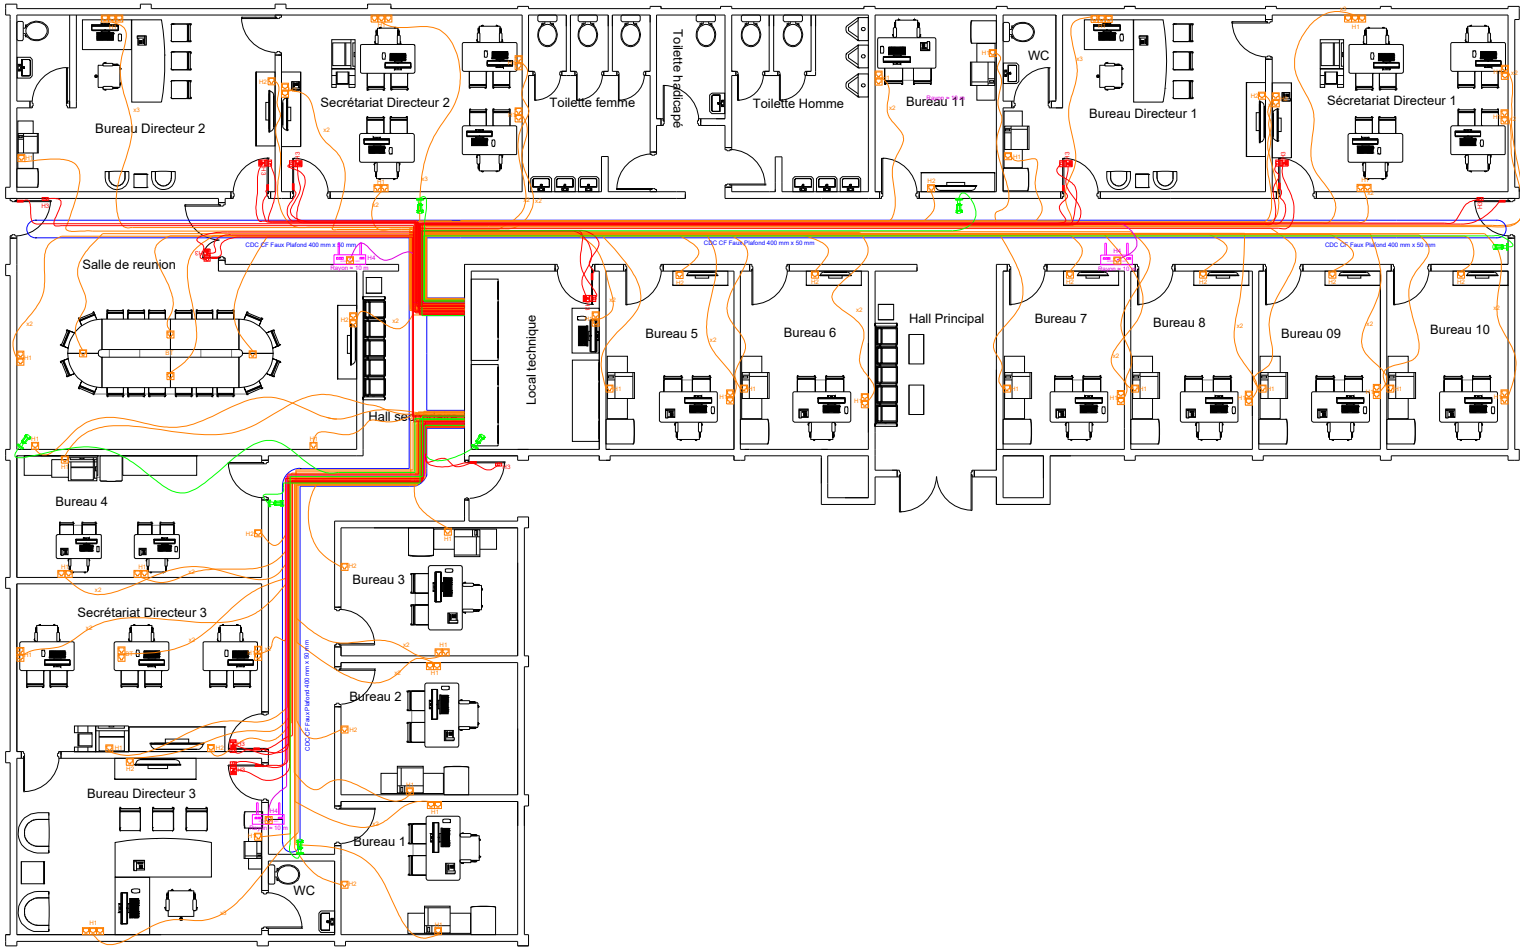

REPUBLIQUE DU CAMEROUN Plateau - Yaoundé - Pointe REPUBLIC OF CAMEROON Yaoundé - Plateau - Pointe REGION DE L'OUEST DEPARTEMENT DE LA MENOUA	
TITRE DU PROJET: PROJET RESEAU & TELECOM EXTENSION BATIMENT DG	
MAITRE D'OUVRAGE :	
MAITRE D'OEUVRE : M. LEONEL DUTROCHET FOTSING	
ENTREPRISE : ETS SCIENCIA BUSINESS GROUP Tel: (+237) 222 31 66 89/ 655 09 54 79 / 681 91 21 20 N° RCCM RC/YAO/2021/A/97 - N.U.I: P059515412618F B.P. Yaoundé - Cameroun, Biyem Assi - Somatel	
 Société spécialisée dans les services d'ingénierie et de prestation de services dans le domaine de l'Informatique et des Télécommunications	
	ACCESS POINT
	PORT RJ45
	LECTEUR DE BADGE
	BOUTON INTERIEUR DE SORTI
	CONTACT DE PORTE
	CAMERAS
LÉGENDE DES HAUTEURS - SOL FINI	
H1	0.3 m
H2	1.5 m
H3	1.10 m
H4	2.50 m
LISTING – RÉSEAU INFORMATIQUE	
UNITE	QUANTITE
Prises RJ45 Cat6 murales	115
Câbles Ethernet Cat6	1336 m
Panneaux de brassages	05
Switch PoE 24 ports	05
Baie de brassage 19"	01
Cordons de brassage	110
Access Point Wi-Fi	03
LISTING – VIDÉOSURVEILLANCE	
UNITE	QUANTITE
Caméras IP PoE	07
Switch PoE dédié caméras	01
NVR (enregistreur vidéo réseau)	01
Disques durs NVR	02
Câbles RJ45 Cat6 caméras	230 m
LISTING – CONTRÔLE D'ACCÈS	
UNITE	QUANTITE
Contrôleur d'accès (04 portes)	03
Lecteurs de badge	08
Boutons de sortie (RTE)	11
Contacts de porte	11
Câbles multi-conducteurs CF	610 m